



Схема укладки площадки

Щебень, три пути колеи 1520 мм, шпалы Ш1, рельс Р65. Размеры в метрах.


План

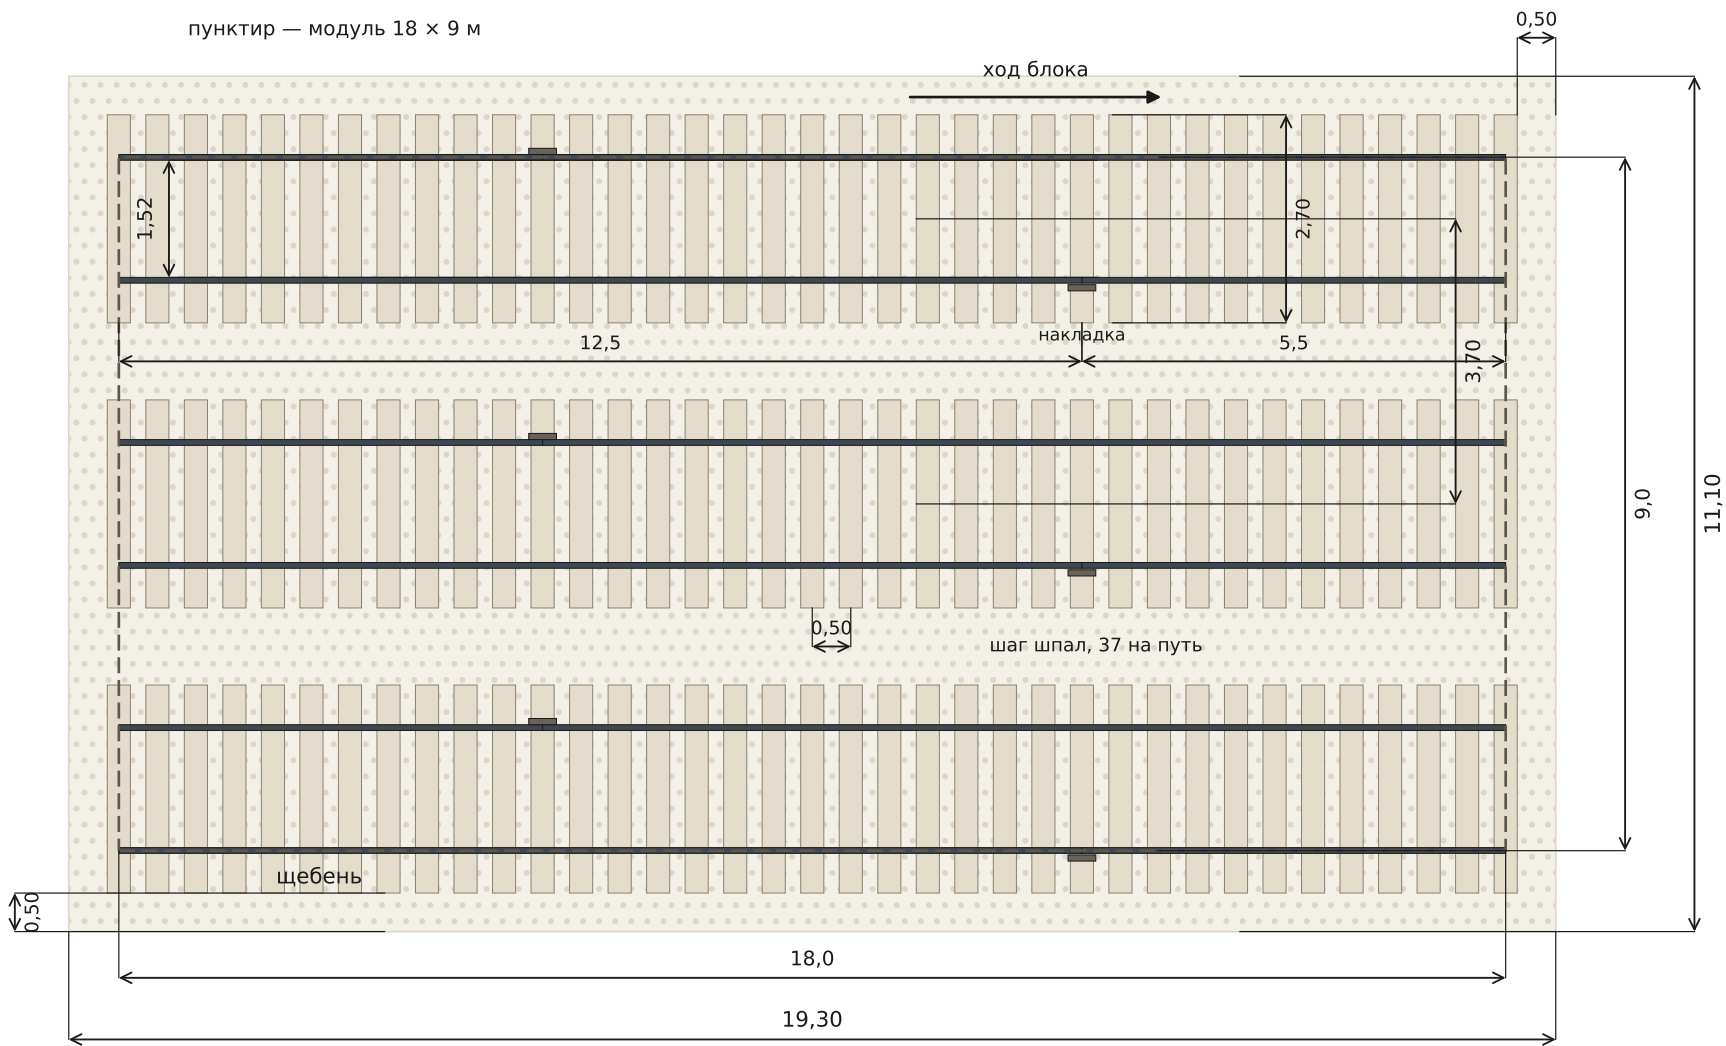

Разрез поперёк путей

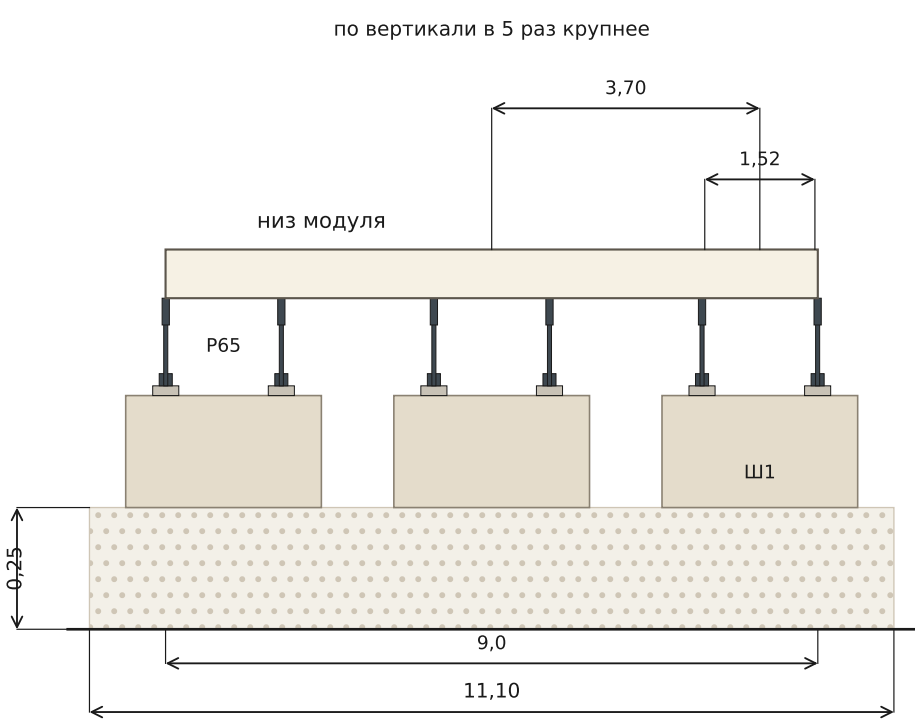

Узел рельса

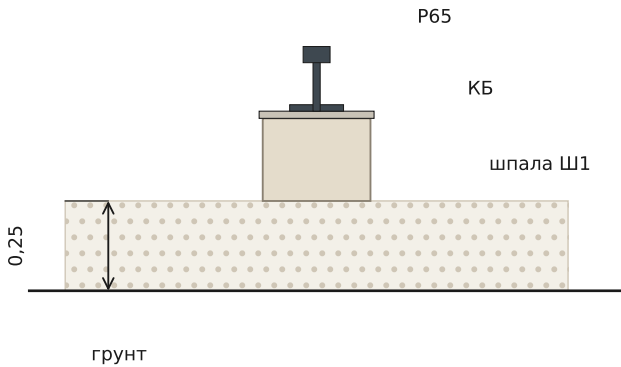

- Площадка 19,30 × 11,10 м.
Щебень фракции 20–40, слой 250 мм в уплотнённом теле. Площадь 214 м².
К заказу 70 м³.
Берма за шпалой 0,50 м.
- Три отдельных пути. Колея каждого 1520 мм — между внутренними гранями головок. Расстояние между осями путей 3,70 м.
- Рельс Р65. Нить 18,0 м складывается из 12,5 м и 5,5 м. В деле 6 × 18 м = 108 м. Заказ: 9 рельсов по 12,5 м. Накладок 6 комплектов. Стыки соседних рельсов разведены.
- Шпала Ш1 под скрепление КБ, длина 2,70 м. Шаг 0,50 м: 37 шпал на путь, всего 111. Подкладок КБ 222.
- Модуль 18 × 9 м опирается на головки. По щебню и по грунту его не тащат.